ROTAŞ MÜHENDİSLİK PROJE MÜŞAVİRLİK

Makine Mühendisliği - Asansör Avan Projesi

HASAN KAYA MİM. MÜH. MOB. VE OTO. İNŞ. TAAH. LTD. ŞTİ.

D BLOK - MAKİNE DAİRESİZ ÇİFT ASANSÖR AVAN PROJESİ

ASANSÖRÜN ÖZELLİKLERİ

İL	SAKARYA	BEYAN YÜKÜ	800 kg (10 kişi) x 2 adet
İLÇE	ADAPAZARI	BEYAN HIZI	1,00 m/s
MAHALLE	KORUCUK	SEYİR MESAFESİ	16,15 m
ADA / PARSEL	3346 / 13	DURAK SAYISI	6 (BODRUM, ZEMİN, 1. KAT, 2. KAT, 3. KAT, 4. KAT)
YİBF	2606440	KUYU ÖLÇÜSÜ (kaba)	215x190 + 200x190
KAT ADEDİ	6	KUYU NET (sıva/kiriş)	200.0x185.0 + 195.0x185.0
ASANSÖR TİPİ	MAKİNE DAİRESİZ	KABİN ÖLÇÜSÜ	1200x1500 mm
ASANSÖR SAYISI	2	KAPI	900x2100 teleskopik otomatik
ASKI TİPİ	2/1	RAY (kabin / K.A.)	T89/B / T50
MOTOR	7,5 kW dişlisiz (gearless)	SON DÖŞEME (motor asma)	alt +17,45 / min 20 cm BA
KUYU DİBİ	1,50 m (kot -4,65)	KUYU ÜST BOŞLUĞU	4,45 m


PROJE MÜELLİFİ	ADI SOYADI	ODA SİCİL NO	İMZA
Makine Mühendisi			
Elektrik Mühendisi			

AVAN TASLAK - mimari ve statik ile koordinasyon notları hesap paftasındadır.

ROTAŞ MÜHENDİSLİK PROJE MÜŞAVİRLİK Makine Mühendisi	HASAN KAYA MİM. MÜH. MOB. VE OTO. İNŞ. TAAH. LTD. ŞTİ. D BLOK - MAKİNE DAİRESİZ ASANSÖR AVAN PROJESİ	
KAPAK / ASANSÖR ÖZELLİKLERİ ÖLÇEK : 1/50	Ada 3346 / Parsel 13 - KORUCUK / ADAPAZARI Tarih: 12.10.2026 Avan - Taslak	A-01

1. KAT PLANI - ASANSÖR KONUMU (mimariden, Ölçek 1/100)

Kırmızı çarpı: asansör kuyuları. Kuyulardan asansöre ait olmayan boru/hat geçmez; kuyu dibine pis su bağlantısı yapılmaz.

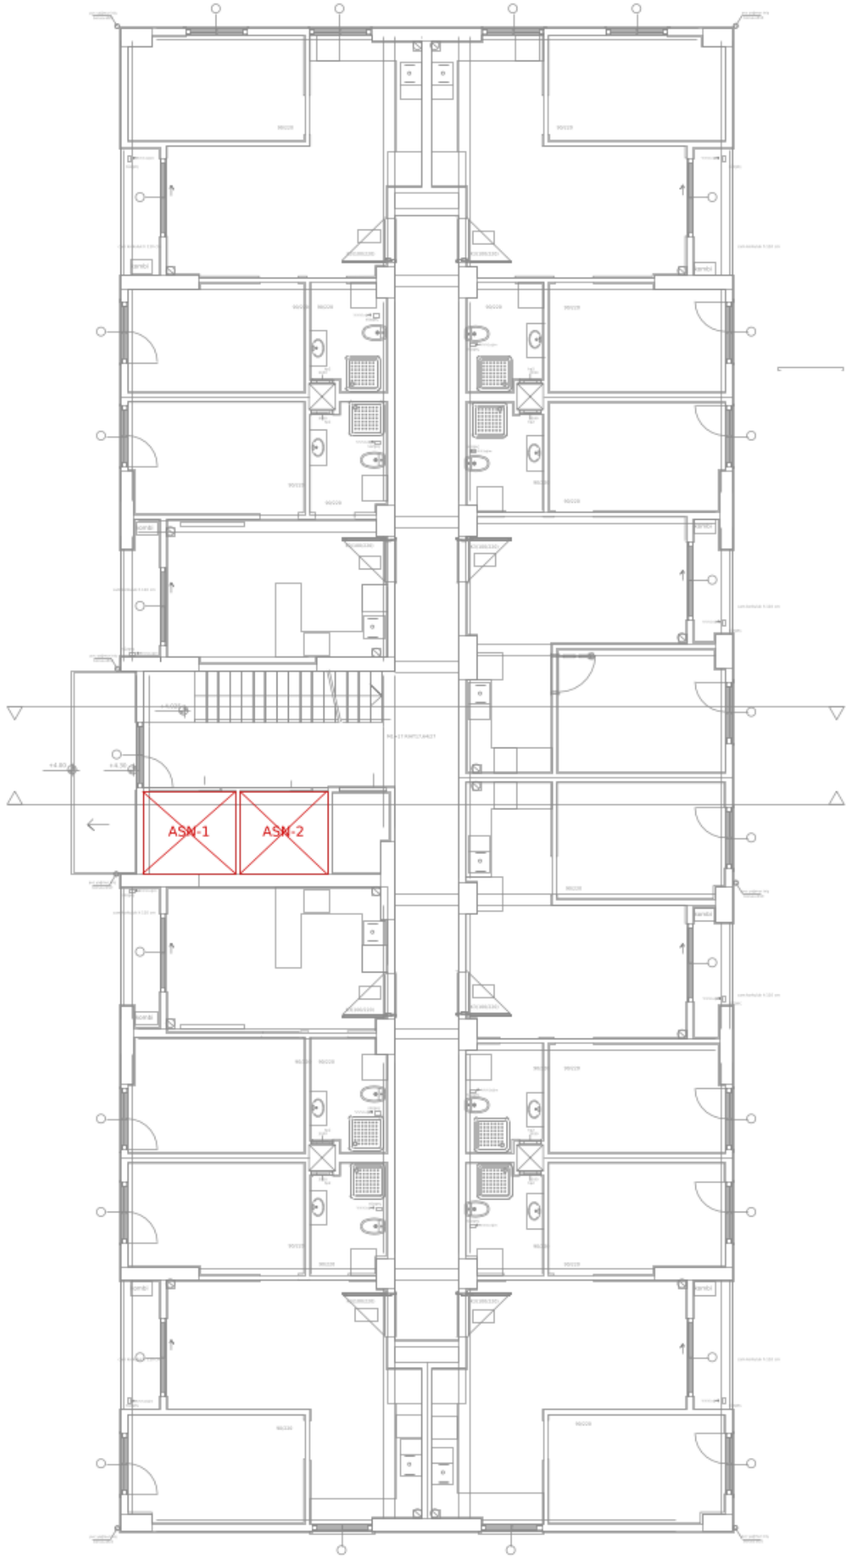

ROTAŞ MÜHENDİSLİK PROJE MÜŞAVİRLİK Makine Mühendisi	HASAN KAYA MİM. MÜH. MOB. VE OTO. İNŞ. TAAH. LTD. ŞTİ. D BLOK - MAKİNE DAİRESİZ ASANSÖR AVAN PROJESİ	
ASANSÖR KONUM PLANI - 1. KAT PLANI ÖLÇEK : 1/100	Ada 3346 / Parsel 13 - KORUCUK / ADAPAZARI Tarih: 12.10.2026 Avan - Taslak	A-02

GİRDİLER (mimariden)

Daireler: 8 adet 1+1, 24 adet 2+1 -> Σb = 120 kişi (Tablo-1: ilk yatak odası 2, diğer odalar 1)

Durak kotları: BODRUM -3,15, ZEMİN 0,00, 1. KAT 4,00, 2. KAT 7,00, 3. KAT 10,00, 4. KAT 13,00 Seyir = 16,15 m

Ana durak: Zemin kat. Ana durak üzerindeki kat sayısı N = 4 (bodrum durağı hesaba katılmaz)

Ortalama kat yüksekliği h = seyir / (durak-1) = 3,23 m. Asansör sayısı n = 2 (çift asansör)

1. ASANSÖR AVAN PROJESİ

1.1. ASANSÖR TRAFİK HESABI

Binada bulunan toplam insan sayısı B = Σb + n·Σb = 120 + 30%·120 = 156,0 kişi

Ana durak üzerindeki kat adedi N = 4 Kabin kapasitesi = 10 kişi (800 kg)

P = %80 doluluk = 0,8 x 10 = 8,0 kişi

H = Ortalama en yüksek dönüş katı = 3,94

S = Ortalama durak adedi = 3,77

V = Kabin hızı = 1,00 m/s h = Katlar arası mesafe = 3,23 m

tv = h / V = 3,23 s

ts = ta + tk + tg - tv = 2,5 + 3,8 + 7,0 - 3,23 = 10,07 s

tp = Kişi transfer zamanı = 2,2 s

1.1.1. Asansörün Bir Seferi İçin Gerekli Seyir Zamanı

T = 2·H·tv + (S+1)·ts + 2·P·tp = 2 x 3,94 x 3,23 + (3,77 + 1) x 10,07 + 2 x 8,0 x 2,2 = 108,8 s

1.1.1.2. Gerekli Asansör Sayısının Hesabı

R = 5 x 60 x P / T = 300 x 8,0 / 108,8 = 22,07 kişi (5 dakikada bir asansörün taşıdığı)

L = B x k / R = 156,0 x 0,075 / 22,07 = 0,53 -> 2 adet asansör

1.1.1.3. Bekleme Zamanı

I = T / n = 108,8 / 2 = 54,4 s ≤ 100 s uygundur.

10 kişilik 1,00 m/s hızında 2 adet asansör seçilmesi uygundur.

ROTAŞ MÜHENDİSLİK PROJE MÜŞAVİRLİK Makine Mühendisi	HASAN KAYA MİM. MÜH. MOB. VE OTO. İNŞ. TAAH. LTD. ŞTİ. D BLOK - MAKİNE DAİRESİZ ASANSÖR AVAN PROJESİ	
HESAP-1 TRAFİK HESABI ÖLÇEK : 1/50	Ada 3346 / Parsel 13 - KORUCUK / ADAPAZARI Tarih: 12.10.2026 Avan - Taslak	A-03

1.2. ASANSÖR KUVVET HESABI

Gk (kabin kütlesi) = 550 kg Gy (beyan yükü) = 800 kg q = 0,5
Karşı ağırlık = Gk + q·Gy = 550 + 0,5 x 800 = 950 kg
Halat kütlesi Gh = gh x lh x nh = 0,373 x 44,2 x 4 = 65,9 kg

1.2.1. Kuyu Alt Boşluğu Tabanına Gelen Kuvvetler

P1 (kabin tamponu altı) = 4 x gn x (Gk + Gy) = 4 x 9,81 x (550 + 800) = 52.974 N
P2 (karşı ağırlık tamponu altı) = 4 x gn x Gka = 4 x 9,81 x 950 = 37.278 N

1.2.3. Kuyu Üstü Betonuna Etki Eden Kuvvetler

F = gn x (Gmakina + Gsehpa + Gmontör + Gk + Gy + Gh + Gka) = 9,81 x (320 + 100 + 150 + 550 + 800 + 66 + 950) = 28.802 N

1.2.4. Asansör Motor Gücü Hesabı

Smaks (artan yük) = Gk + Gh + Gy - Gka = 466 kg M = Smaks x D/2 = 55,9 kg.m
N = (1/η) x S x V / 102 = (1/0,80) x 466 x 1,00 / 102 = 5,71 kW (7,7 HP) -> seçilen 7,5 kW
10 kişilik 1,00 m/s hızında 7,5 kW lık 2 adet insan asansörü tesis edilecektir.
ASANSÖR 4 HALATLI, 2/1 ASKILI OLACAKTIR.

KONTROLLER
Kabin alanı 1,80 m² ≤ EN 81-20 en büyük 2,00 m² : UYGUN
İmar (dar kenar ≥ 1,20 m, alan ≥ 1,80 m², kapı ≥ 0,90 m): UYGUN
Eski TS yöntemi çapraz kontrol: TR=58,2 s, N=5,16 sefer/5dk, B3=103,1 > B2=9,0 : UYGUN
Kuyu mesafesi ≈ kuyu dibi 1,50 + seyir 16,15 + kuyu üstü 4,45 = 22,10 m

KUYU İÇ ÖLÇÜLERİ VE SON DÖŞEME KONTROLÜ (mimariden ölçülmüştür)

Kuyu ölçüleri (kaba / sıvalı): kuyu 200 / ~195 (sıva çizilmemiş) ; kuyu 215 / kiriş yüzü 200 (bodrumda kuyu 200) ; derinlik 190 / ~185. Tüm katlarda aynı yerde ve aynı ölçüde.
Kiriş kuyu içine taşıyor: o kuyuda net genişlik kiriş yüzüyle sınırlı. Kiriş kuyu yüzüne çekilmeli ya da net ölçü esas alınmalı.
Esas alınan net ölçü (her iki kuyu): ~195 x 185 cm. Kabin 1200x1500 + yan karşı ağırlık sığıyor, derinlik sıkı: firma teyidi gerekir.
Motorun asıldığı son döşeme: alt kotu +17,45, mimaride 10 cm. Son durak +13,00 -> kuyu üst boşluğu 4,45 m (yeterli). Döşeme min 20 cm BA + askı kancası.
Kuyu dibi: bodrum -3,15 altında 1,50 m -> dip kotu -4,65 (temel üstü -3,75 / alt -4,35 altına iner; statik).
D blok mimarisinde asansör kesiti yok; son döşeme kotu A/B/C ile aynı (+17,45) kabul edildi - teyit edilecek.

KOORDİNASYON NOTLARI

Asansör kuyusundan ve kuyu tavanından asansöre ait olmayan boru/kablo geçmez.
Kuyu dibine pis su süzgeci/bağlantısı yapılmaz; kuyu dibi su yalıtımlı.
Rögar ve altyapı hatları kuyu dibi altından ve asansör kapı önlerinden geçmez.
Ray konsolları için kuyu duvarları betonarme (mimaride 10 cm ara duvar var; perde/hatıl statikle).
Asansör kuyusu ve önü ısıtılmaz; kuyu tavanında duman tahliye açıklığı bırakılır.

ROTAŞ MÜHENDİSLİK PROJE MÜŞAVİRLİK Makine Mühendisi	HASAN KAYA MİM. MÜH. MOB. VE OTO. İNŞ. TAAH. LTD. ŞTİ. D BLOK - MAKİNE DAİRESİZ ASANSÖR AVAN PROJESİ	
HESAP-2 KUVVET / MOTOR / KONTROLLER ÖLÇEK : 1/50	Ada 3346 / Parsel 13 - KORUCUK / ADAPAZARI Tarih: 12.10.2026 Avan - Taslak	A-04

Tablo-1 Binada sürekli insan sayısı (b)

Bina tipi	Bağımsız bölüm	b
Konut	her dairede ilk yatak odası	2
Konut	diğer odaların her biri	1
Otel	her yatak	1
İş merkezi	çalışma alanının her 12 m²si	1
Hastane	her yatak	3

Tablo-2 Kabin hızları

Bina	Durak	V (m/s)
Konut	2-9	1,0
Konut	10-14	1,6
Konut	15-19	2,0
Konut	20+	>=2,5

Tablo-4 Kapı açılma/kapanma zamanları (s)

Kapı mm	Telesk. ta	Telesk. tk	Merkez ta	Merkez tk
700	2,5	3,0	2,0	2,5
800	2,5	3,0	2,0	2,5
900	2,5	3,8	2,3	2,9
1100	3,0	4,0	2,5	3,5
1300	3,7	5,0	2,7	3,7

Tablo-6 Tek katı geçme zamanı

V m/s	<1	1,0	1,6	2,0	2,5	3,5	5,0	>5
tg (s)	10	7,0	6,0	5,7	5,5	5,0	4,5	4,3

Tablo-7 Kabin kapasitesi

Kişi	6	8	10	13	16	20	25	30
kg	450	630	800	1000	1275	1600	2000	2500

Tablo-9 Taşınacak insan yüzdesi (k)

Bina	Standart	Yükseltilmiş
Konut	%7,5	%10
Otel	%12	%15
İş merkezi	%15	%17

Tablo-10 İzin verilen en fazla bekleme zamanı

Sınıf	Şartlı	Standart	Yüks.
Konut	120 s	100 s	80 s
Karma	60 s	50 s	30 s

H ve S değerleri tablo yerine formülle hesaplanmıştır (MMO tablolarıyla aynı sonuç):


H = N - Σ(i/N)^P (i=1..N-1) S = N·[1 - ((N-1)/N)^P]

ROTAŞ MÜHENDİSLİK PROJE MÜŞAVİRLİK Makine Mühendisi	HASAN KAYA MİM. MÜH. MOB. VE OTO. İNŞ. TAAH. LTD. ŞTİ. D BLOK - MAKİNE DAİRESİZ ASANSÖR AVAN PROJESİ	
TABLOLAR ÖLÇEK : 1/50	Ada 3346 / Parsel 13 - KORUCUK / ADAPAZARI Tarih: 12.10.2026 Avan - Taslak	A-05

Kabin ve karşı ağırlık yerleşimi şematiktir; firma uygulama projesinde ray/konsol yerleri kesinleşecektir.


Ray konsolları için kuyu duvarları betonarme perde veya her katta betonarme hatıl olmalıdır (statik).

	ASANSÖR-1	ASANSÖR-2
Kuyu kaba (cm)	215 x 190	200 x 190
Kuyu net (cm)	200.0 x 185.0	195.0 x 185.0
Kabin (mm)	1200 x 1500	1200 x 1500
Kapasite / hız	800 kg / 1,00 m/s	800 kg / 1,00 m/s
Kapı	900 telesk. otomatik	900 telesk. otomatik
Askı / ray	2/1 T89 + T50	2/1 T89 + T50

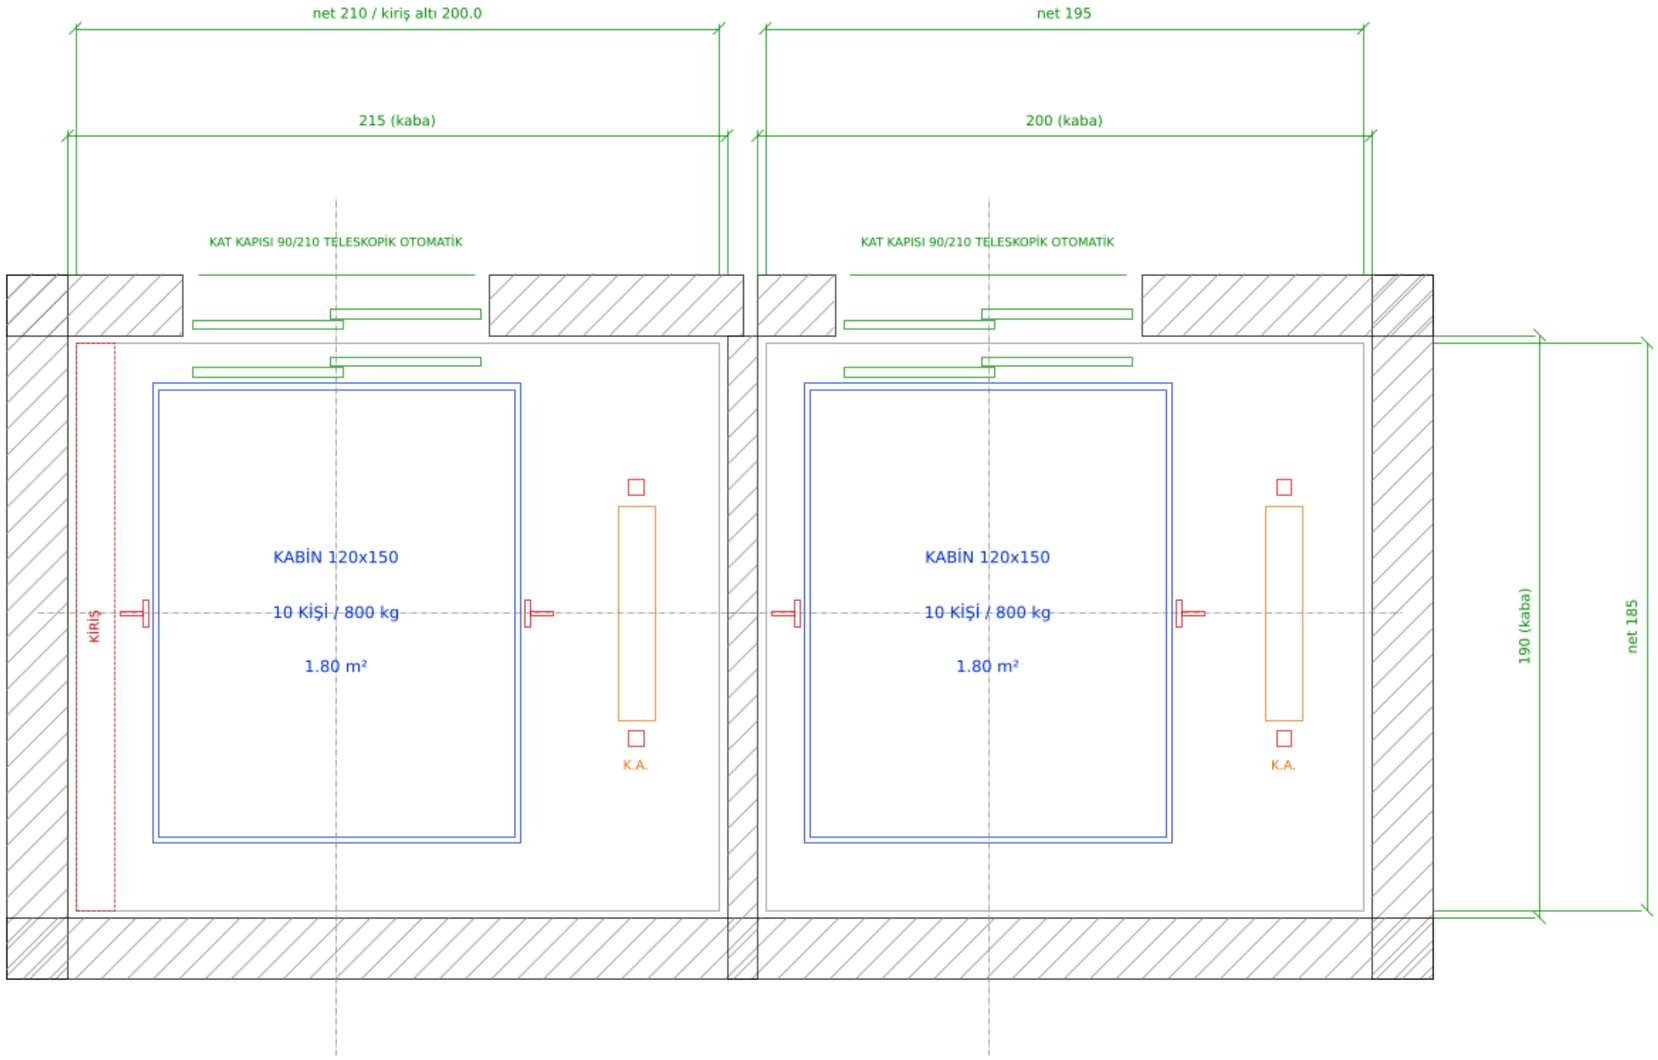

ROTAŞ MÜHENDİSLİK PROJE MÜŞAVİRLİK Makine Mühendisi	HASAN KAYA MİM. MÜH. MOB. VE OTO. İNŞ. TAAH. LTD. ŞTİ. D BLOK - MAKİNE DAİRESİZ ASANSÖR AVAN PROJESİ	
KUYU YERLEŞİM PLANI ÖLÇEK : 1/20	Ada 3346 / Parsel 13 - KORUCUK / ADAPAZARI Tarih: 12.10.2026 Avan - Taslak	A-06

KUYU DİBİ YÜKLERİ (her kuyu) Ö:1/20

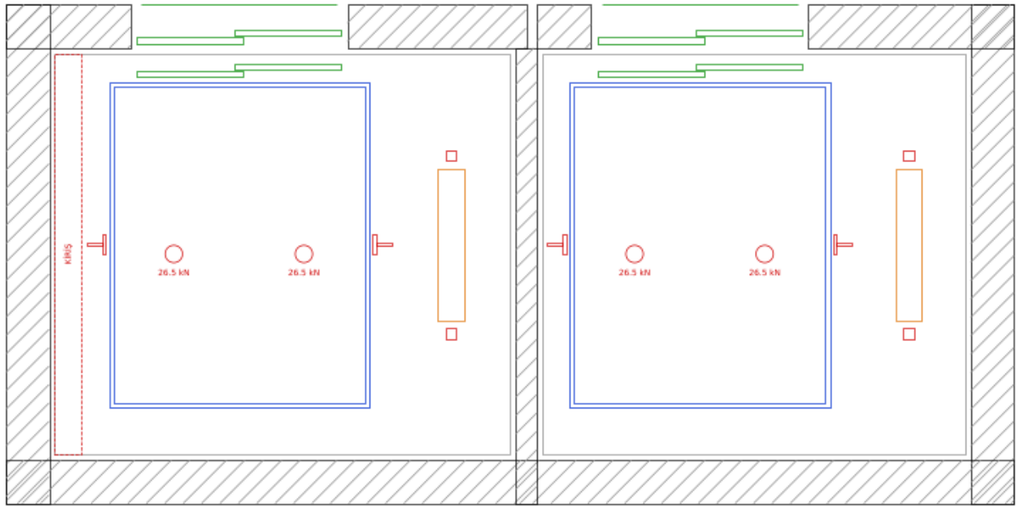

ASANSÖR-1 ASANSÖR-2


Kabin tamponları altı toplam P1 = 4·gn·(P+Q) = 53,0 kN (2 tampon, her biri 26,5 kN)

Karşı ağırlık tamponu altı P2 = 4·gn·(P+q·Q) = 37,3 kN

Kuyu dibi döşemesi kotu -4,65 ; kuyu dibi derinliği 1,50 m (mimaride D mimarisinde asansör kesiti yok).

SON DÖŞEME: alt +17,45 / üst +17,65 - min 20 cm betonarme

MOTORUN ASILDIĞI SON DÖŞEME (KUYU TAVANI) PLANI Ö:1/20

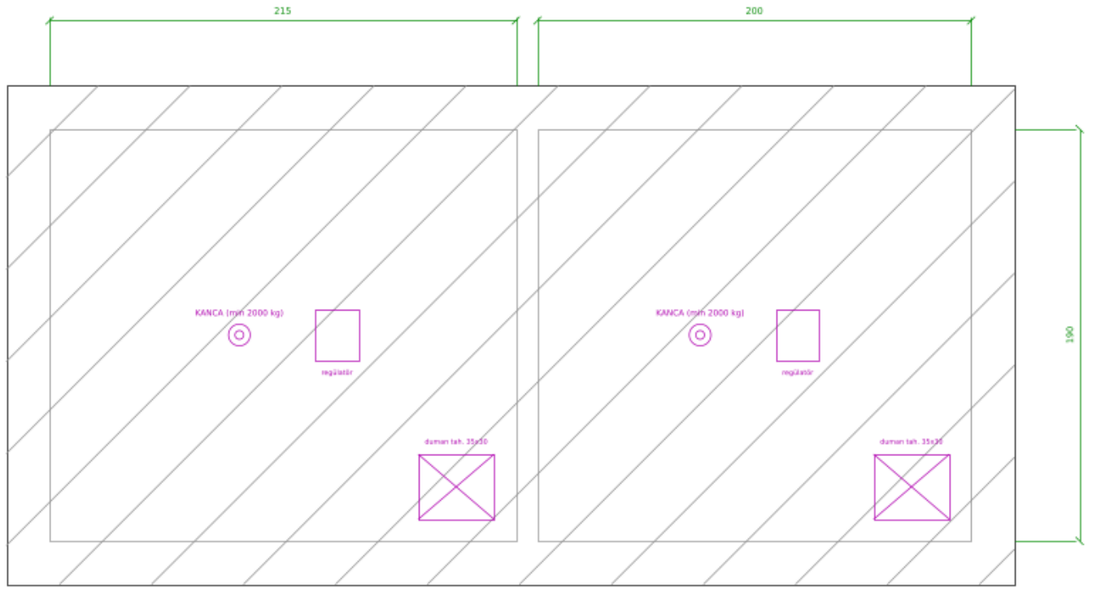

ASANSÖR-1 ASANSÖR-2


Son döşeme alt kotu +17,45 (son durak +13,00 -> kuyu üst boşluğu 4,45 m)
Mimaride döşeme kalınlığı 10 cm -> motor asılacağı için en az 20 cm betonarme (statik hesaplı).
Her kuyu için döşemeye gelen düşey yük F = 28,8 kN (statik); dinamik katsayı statikçe uygulanacak.
Her kuyu tavanına kabin ekseninde montaj/askı kancası; kancanın taşıma kapasitesi üzerine yazılır.
Kuyu tavanında duman tahliye açıklığı (kuyu kesitinin en az %1i) bırakılır.

ROTAŞ MÜHENDİSLİK PROJE MÜŞAVİRLİK Makine Mühendisi	HASAN KAYA MİM. MÜH. MOB. VE OTO. İNŞ. TAAH. LTD. ŞTİ. D BLOK - MAKİNE DAİRESİZ ASANSÖR AVAN PROJESİ	
KUYU DİBİ YÜKLERİ / SON DÖŞEME PLANI ÖLÇEK : 1/20	Ada 3346 / Parsel 13 - KORUCUK / ADAPAZARI Tarih: 12.10.2026 Avan - Taslak	A-07

ASANSÖR KUYUSU DİKİNE KESİTİ - YANDAN GÖRÜNÜŞ

Ölçek 1/50 - Makine dairesiz

Kuyu dibi -4,65 kotunda (mimaride: D mimarisinde asansör kesiti yok).
Son döşeme alt +17,45, min 20 cm BA, motor askı kancalı.
Kuyu dibinde kuyu genişliği daralmayacak (hatıl/temel kirişi içeri taşmaz).
Kuyu dibine pis su süzgeci/bağlantısı konmaz; su yalıtımı yapılır.
Kuyu aydınlatması: kabin tavanı ve kuyu dibinin 1 m üstünde min 50 lüks.

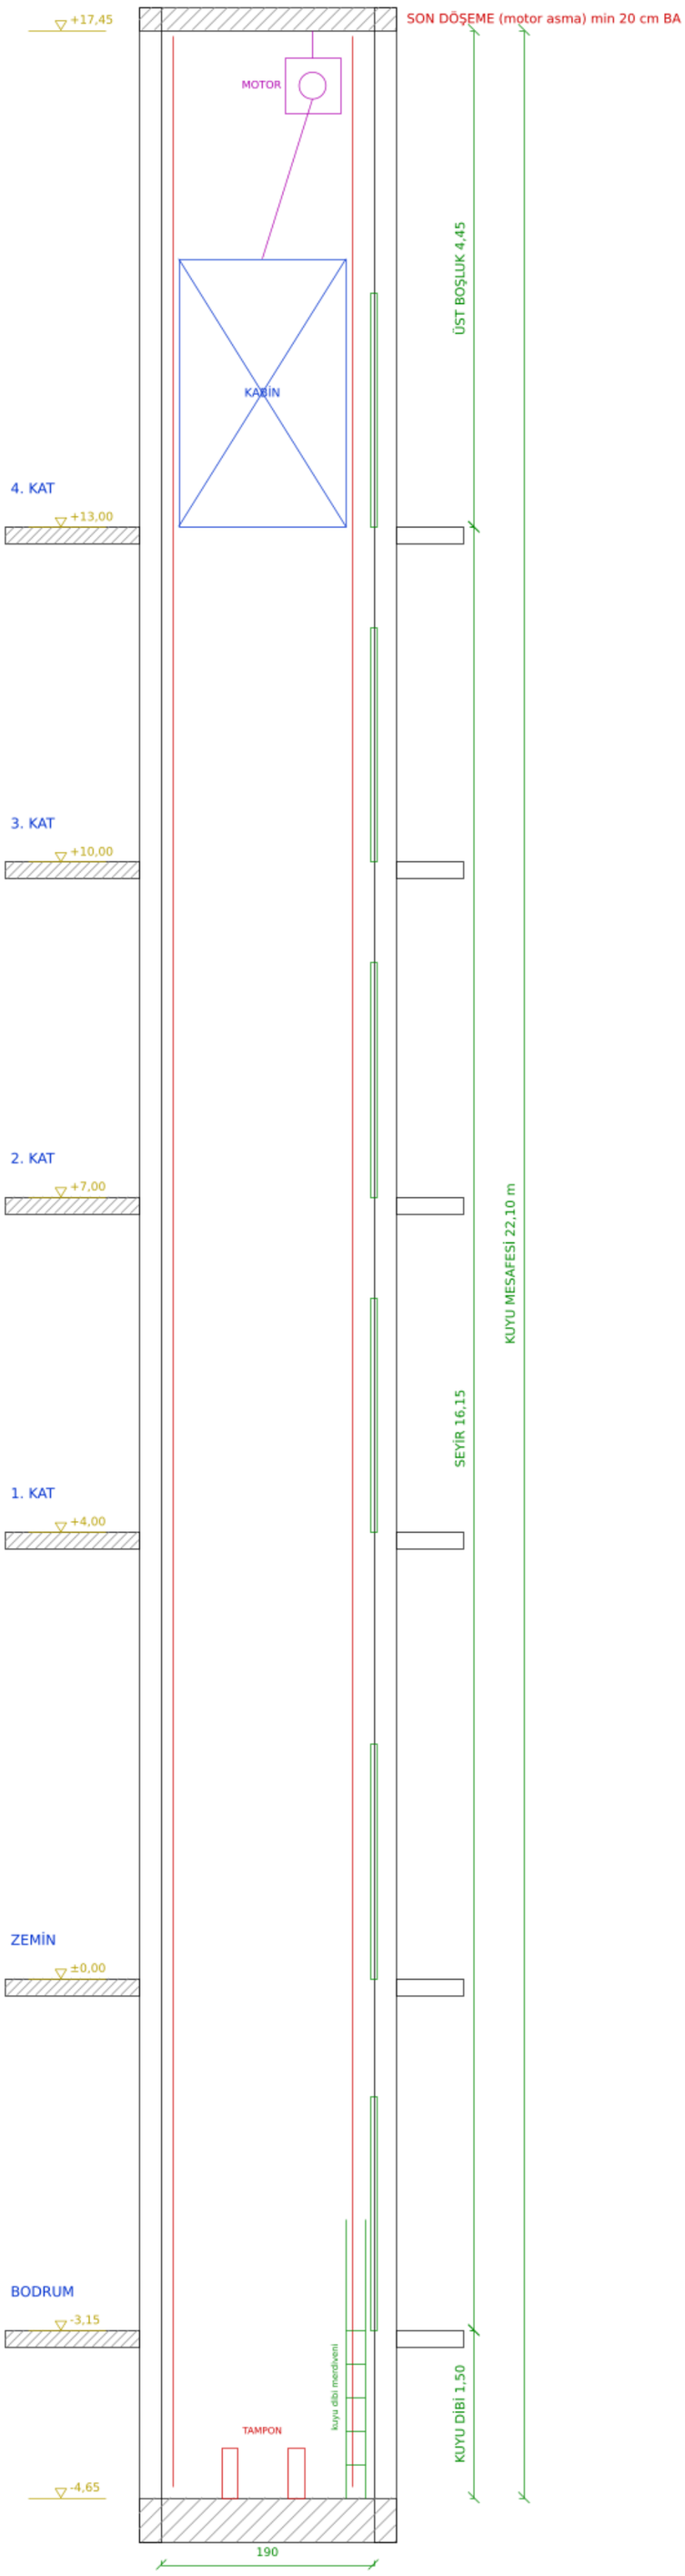


ROTAŞ MÜHENDİSLİK PROJE MÜŞAVİRLİK Makine Mühendisi	HASAN KAYA MİM. MÜH. MOB. VE OTO. İNŞ. TAAH. LTD. ŞTİ. D BLOK - MAKİNE DAİRESİZ ASANSÖR AVAN PROJESİ	
KUYU KESİTİ - YANDAN ÖLÇEK : 1/50	Ada 3346 / Parsel 13 - KORUCUK / ADAPAZARI Tarih: 12.10.2026 Avan - Taslak	A-08


ASANSÖR KUYUSU DİKİNE KESİTİ - KARŞIDAN GÖRÜNÜŞ

Ölçek 1/50 - Makine dairesiz


Kuyu dibi -4,65 kotunda (mimaride: D mimarisinde asansör kesiti yok).
Son döşeme alt +17,45, min 20 cm BA, motor askı kancalı.
Kuyu dibinde kuyu genişliği daralmayacak (hatıl/temel kirişi içeri taşmaz).
Kuyu dibine pis su süzgeci/bağlantısı konmaz; su yalıtımı yapılır.
Kuyu aydınlatması: kabin tavanı ve kuyu dibinin 1 m üstünde min 50 lüks.

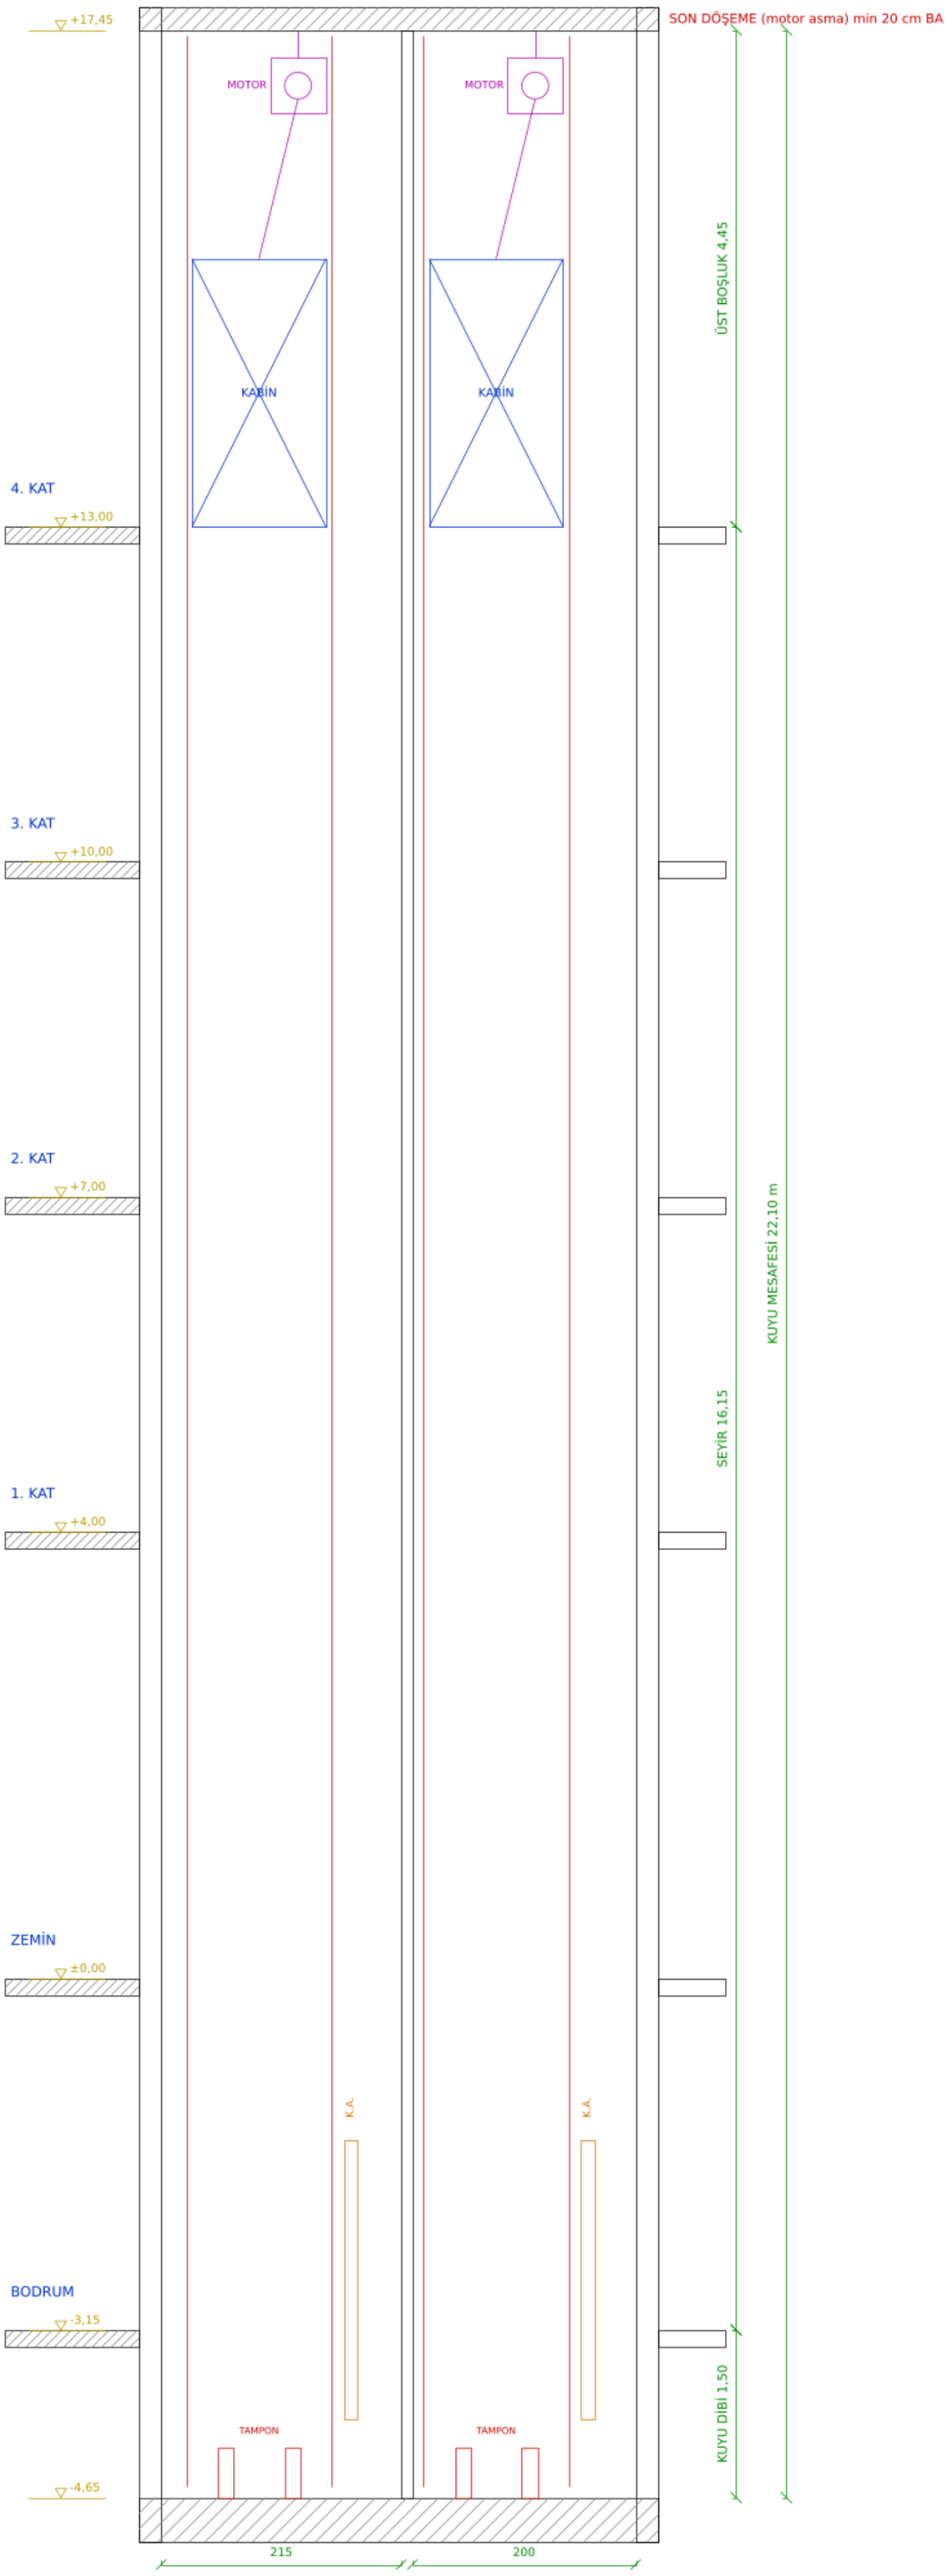

ROTAŞ MÜHENDİSLİK PROJE MÜŞAVİRLİK Makine Mühendisi	HASAN KAYA MİM. MÜH. MOB. VE OTO. İNŞ. TAAH. LTD. ŞTİ. D BLOK - MAKİNE DAİRESİZ ASANSÖR AVAN PROJESİ	
KUYU KESİTİ - KARŞIDAN ÖLÇEK : 1/50	Ada 3346 / Parsel 13 - KORUCUK / ADAPAZARI Tarih: 12.10.2026 Avan - Taslak	A-09

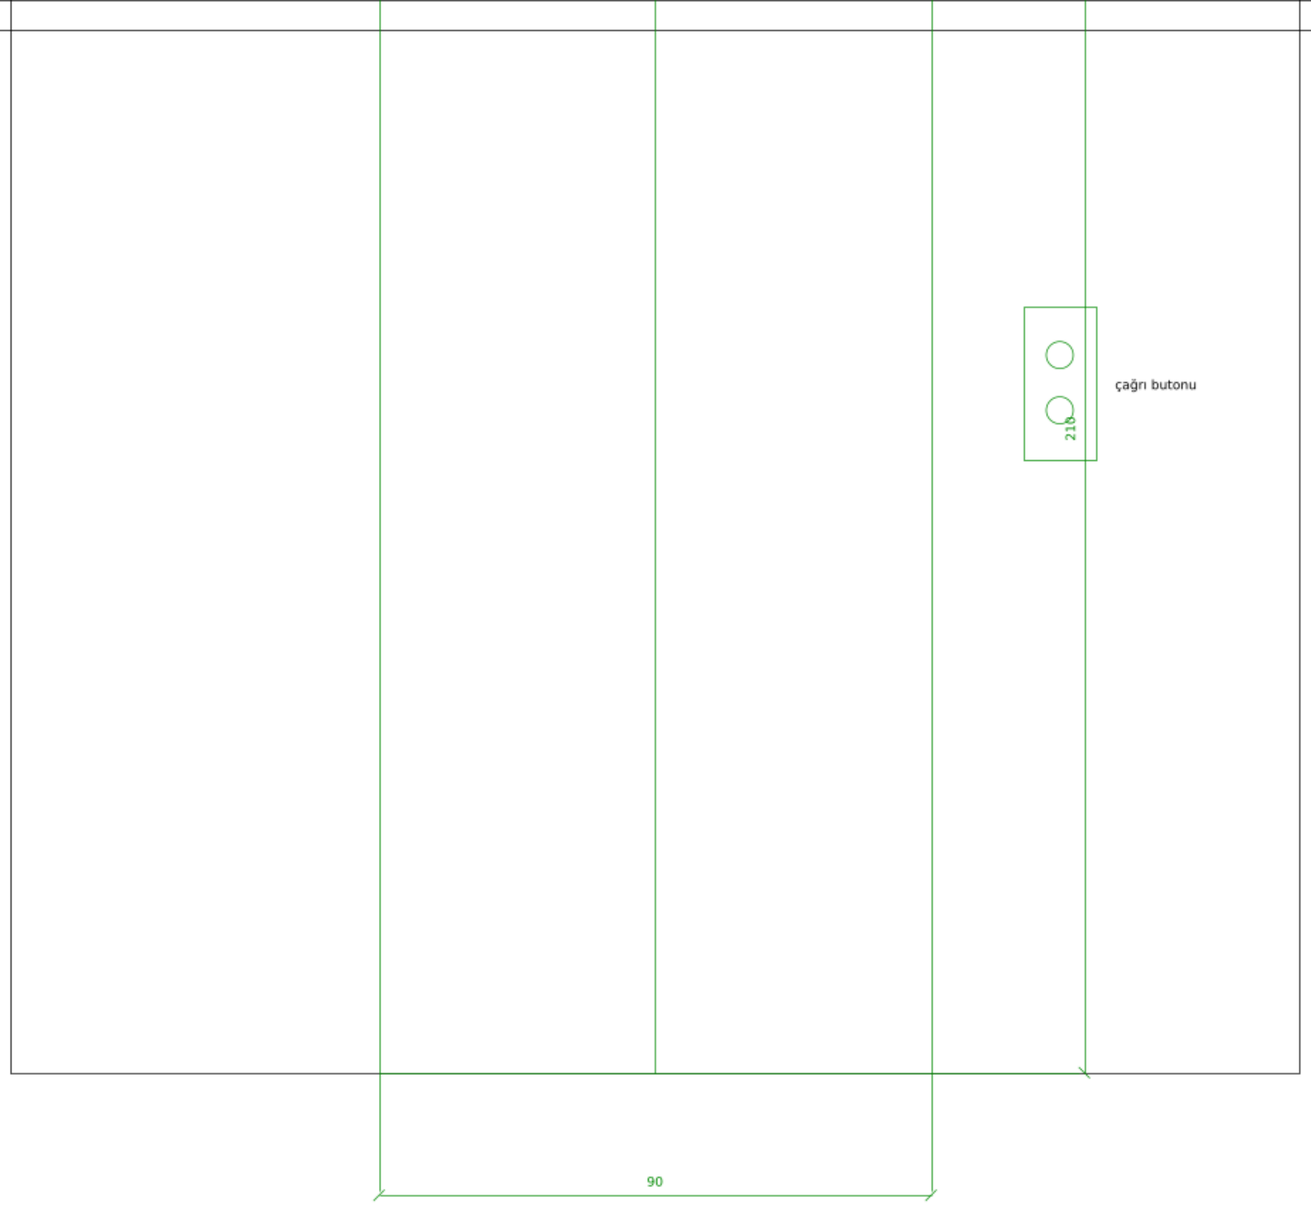

KAT KAPISI GÖRÜNÜŞÜ (teleskopik otomatik, E120/EI60 yangın sınıfı)

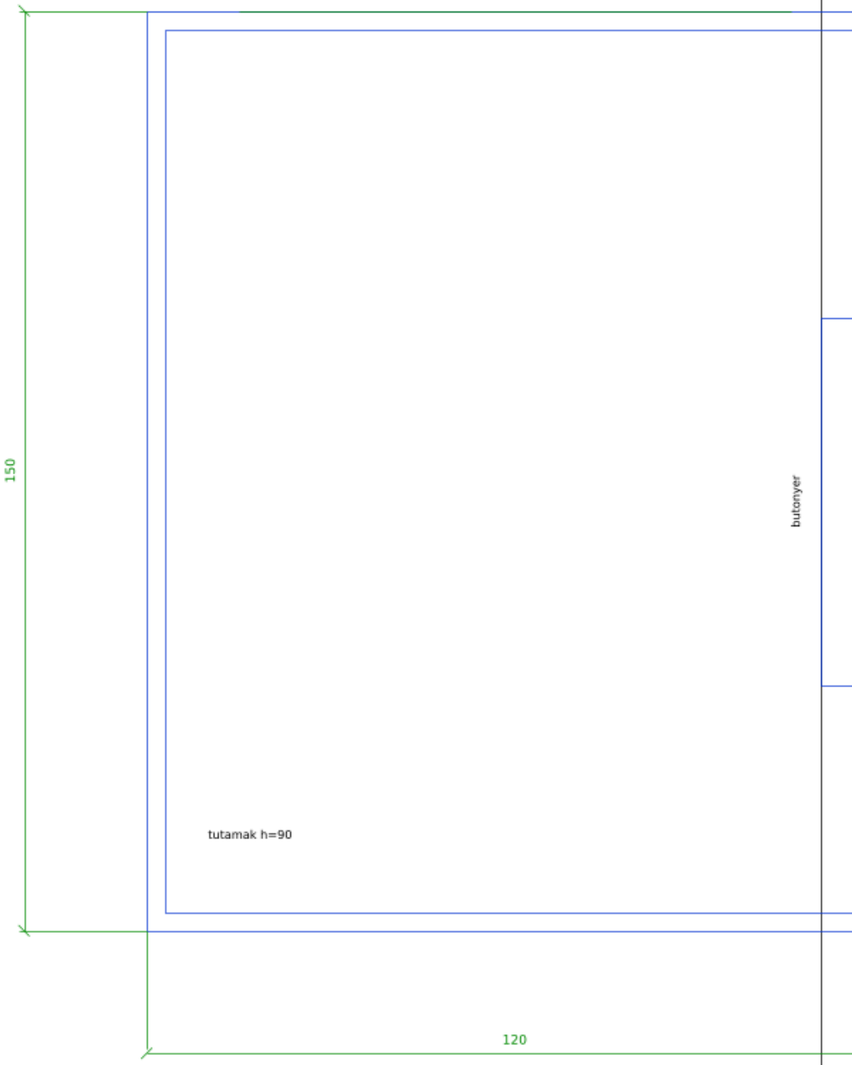

KABİN PLANI 1200x1500 - engelli erişimine uygun

ROTAŞ MÜHENDİSLİK PROJE MÜŞAVİRLİK Makine Mühendisi	HASAN KAYA MİM. MÜH. MOB. VE OTO. İNŞ. TAAH. LTD. ŞTİ. D BLOK - MAKİNE DAİRESİZ ASANSÖR AVAN PROJESİ	
KAT KAPISI / KABİN / BUTONYER DETAYLARI ÖLÇEK : 1/10	Ada 3346 / Parsel 13 - KORUCUK / ADAPAZARI Tarih: 12.10.2026 Avan - Taslak	A-10